

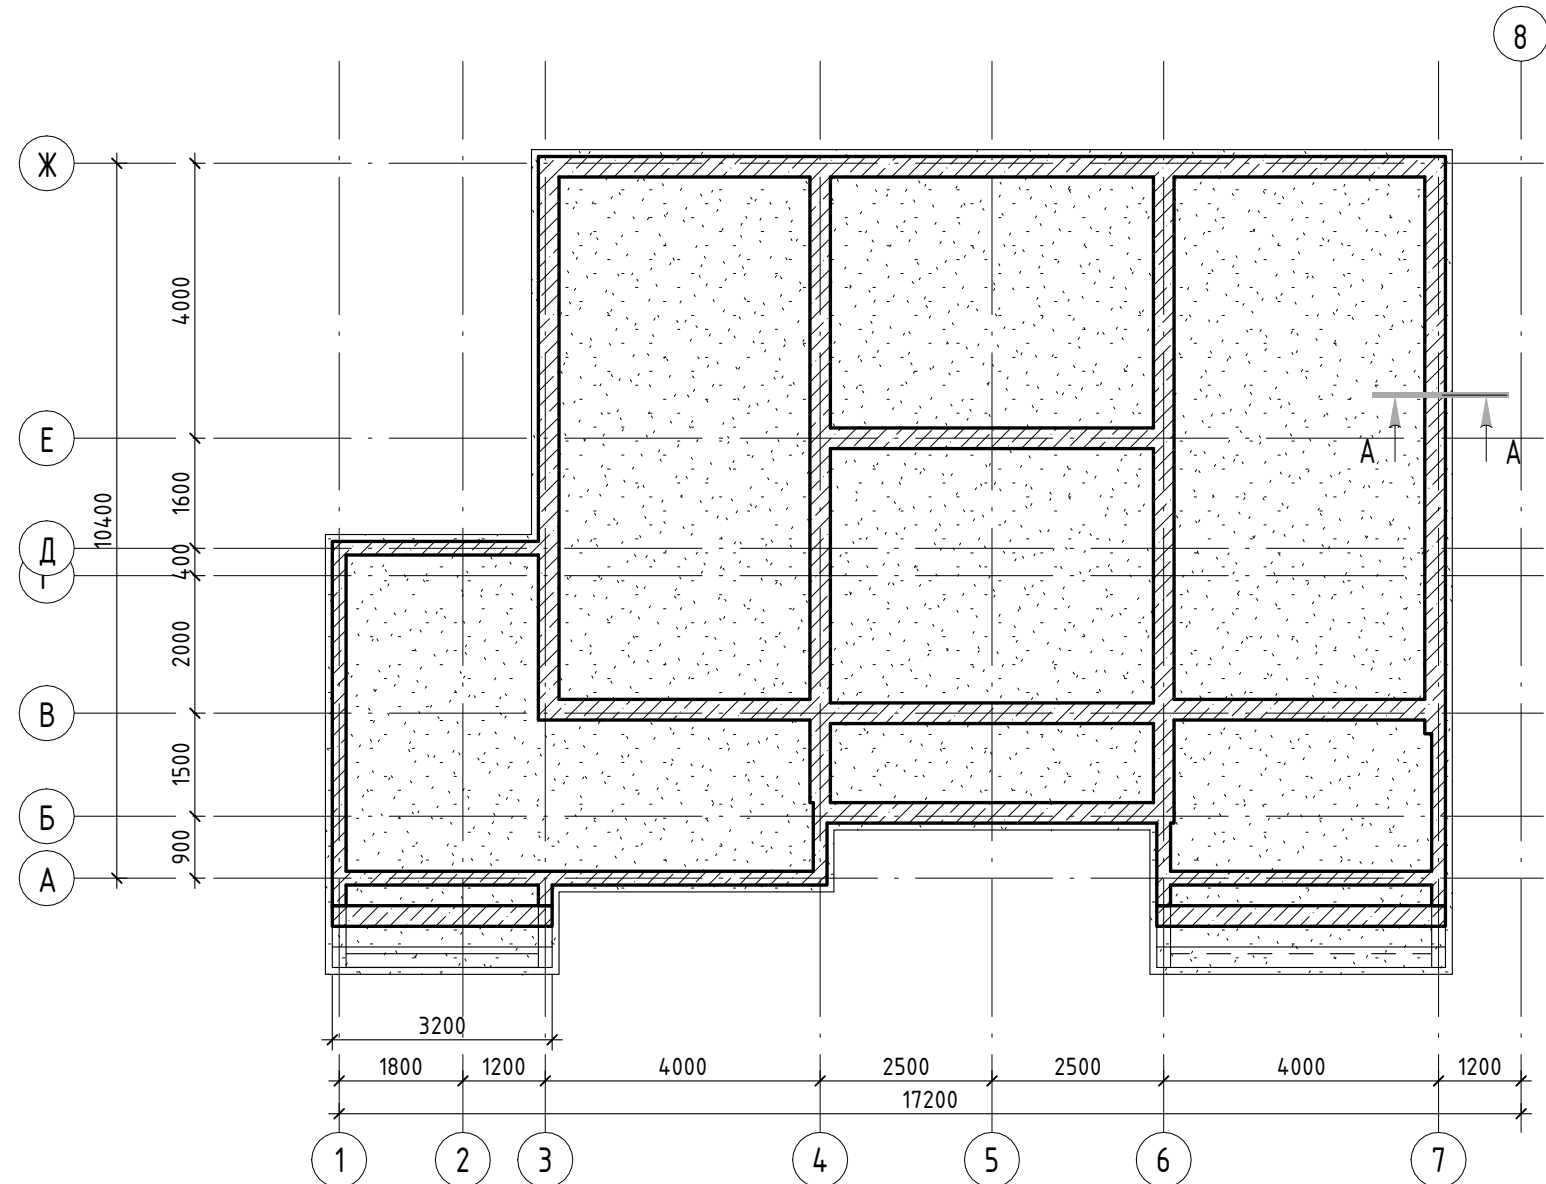


Согласовано					
Согласовано					
Инв. № подл.	Изм. №	Подп. и дата	Взам. инв. №		

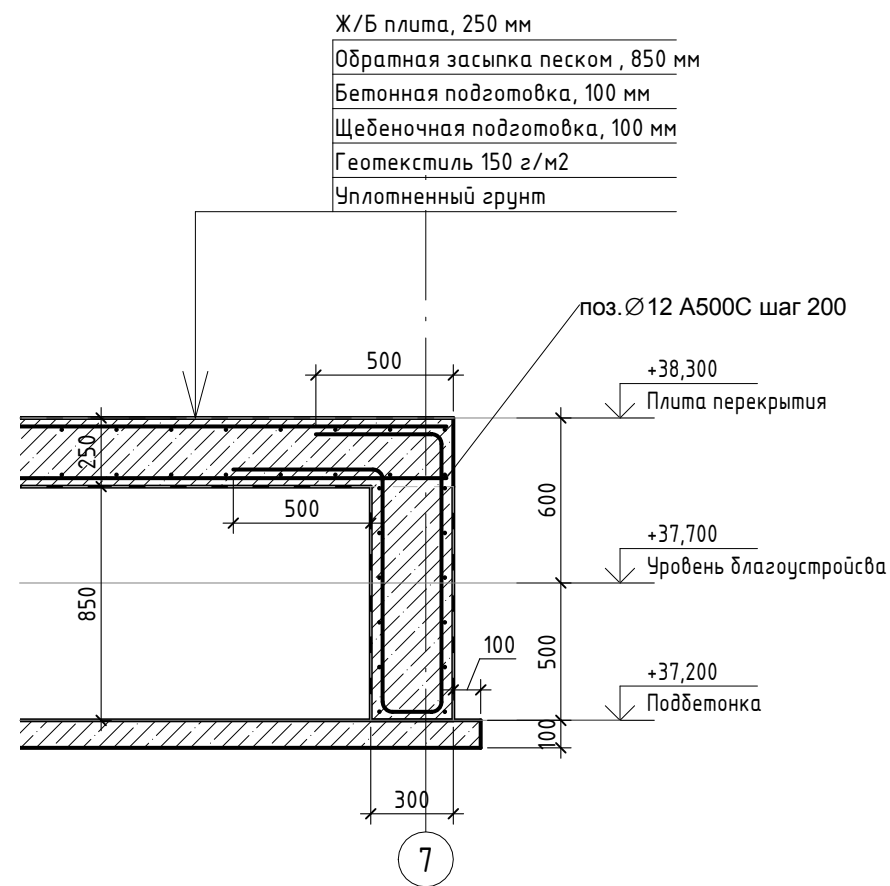

						ДСП № 12/08-РП-15 - КЖ		
						Ленинградская область, Приозерский муниципальный район		
Изм.	Кол.уч.	Лист	№ док.	Подп.	Дата	Индивидуальный жилой дом.	Стадия	Лист
Разработал		Мисак					П	01
Проверил		Базров				Схема бетонирования фундамента	000 "Аракс"	

Инв. № подл.	Подп. и дата	Взам. инв. №	Согласовано					

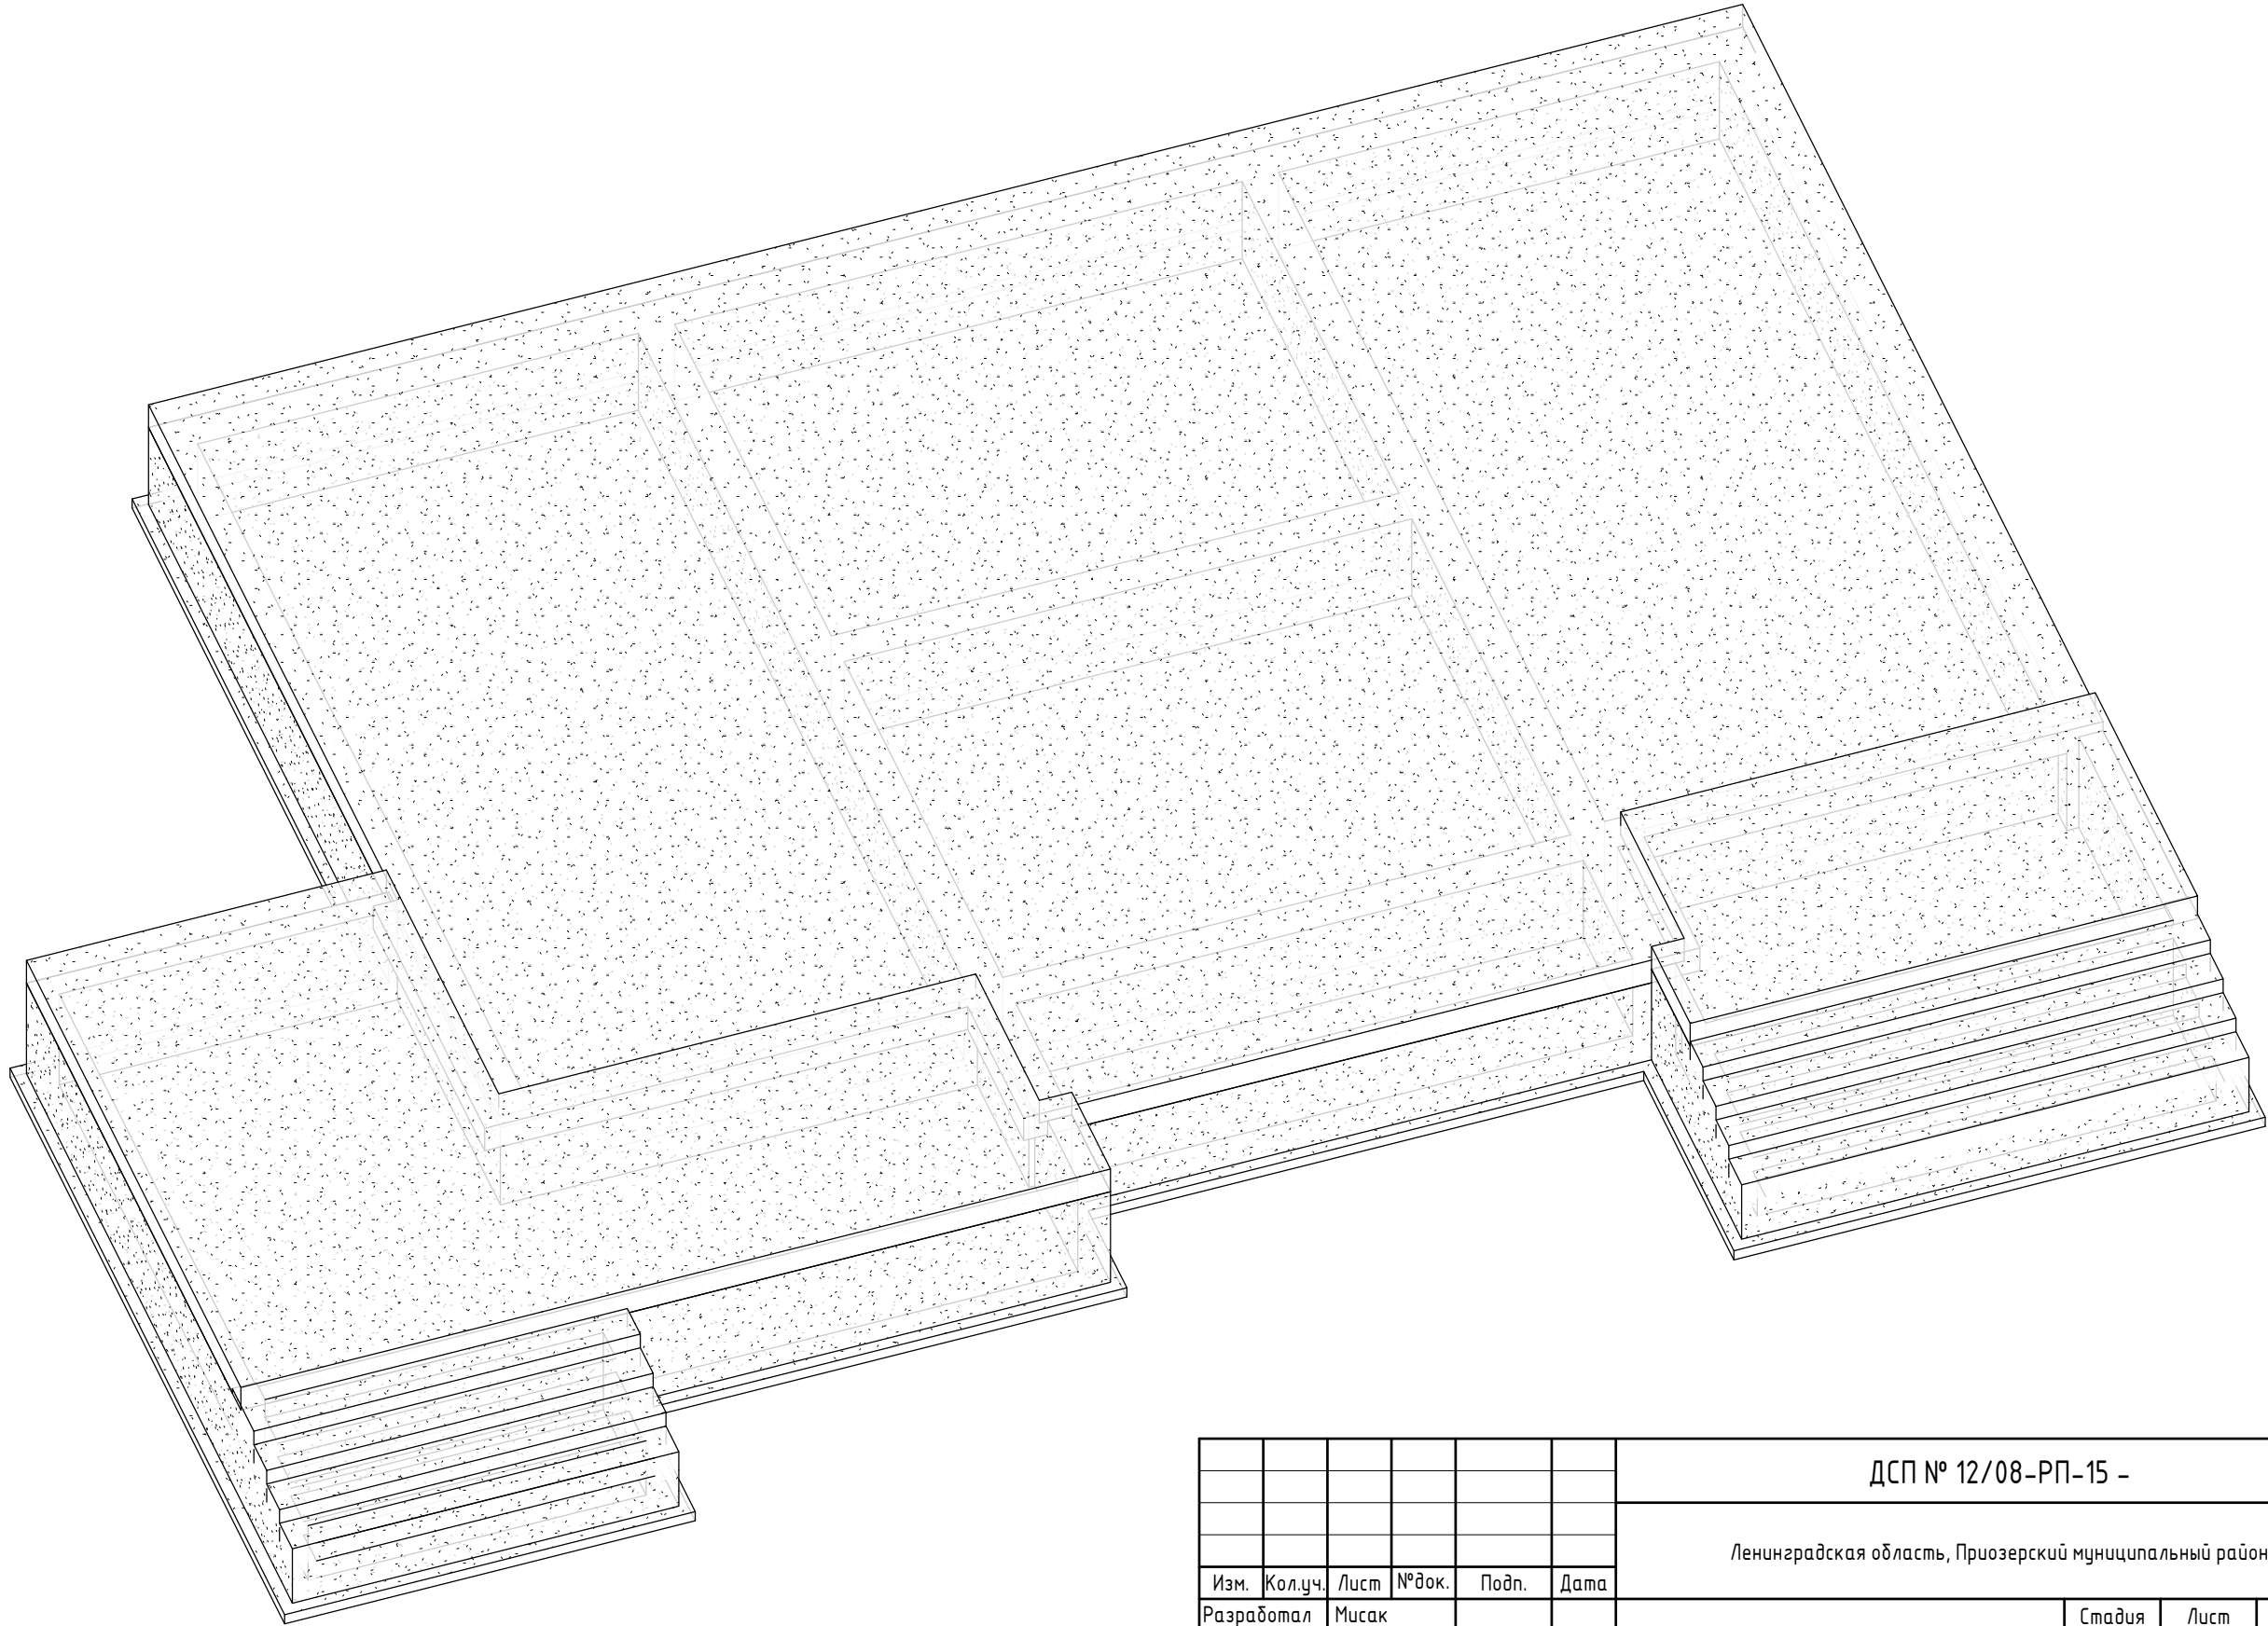

						ДСП № 12/08-РП-15 -			
						Ленинградская область, Приозерский муниципальный район			
Изм.	Кол.уч.	Лист	№ док.	Подп.	Дата	Индивидуальный жилой дом.	Стадия	Лист	Листов
Разработал		Мисак					П	02	
Проверил		Базров							
						Фундамент 3D Вид	ООО "Аракс"		