


№ пп	Наименование	Диаметр трубы/Сечение кабеля	Длина/Количество
1	Бытовая канализация КБ		
1.1	труба наружная, м	Ø110	34
2	Канализация (очищенная) К1-1		
2.1	труба наружная, м	Ø110	17
3	Ливневая канализация К2-1		
3.1	труба наружная, м	Ø110	83
3.2	труба наружная, м	Ø160	32
3.3	труба наружная, м	Ø200	55
3.4	Колодец смотровой, шт		7
4	Водопровод В1		
4.1	труба ПНД, м	Ø32	135
4.2	Колодец смотровой, шт		1
5	Эл. кабель 0,4 Кв		
5.1	кабель, м	10 мм2	46
5.2	кабель, м	4 мм2	389


				ДСП № 12/08-РП			
Должность	Ф.И.О.	Подпись	Дата	Адрес: Ленинградская область, Приозерский муниципальный округ			
Ген. дир.	Анциловский			Индивидуальный жилой дом	Стадия	Лист	Листов
Гл. инж.	Базров				П		
Геодезист	Мисак						
				Сводный план сетей		ООО "Аракс"	

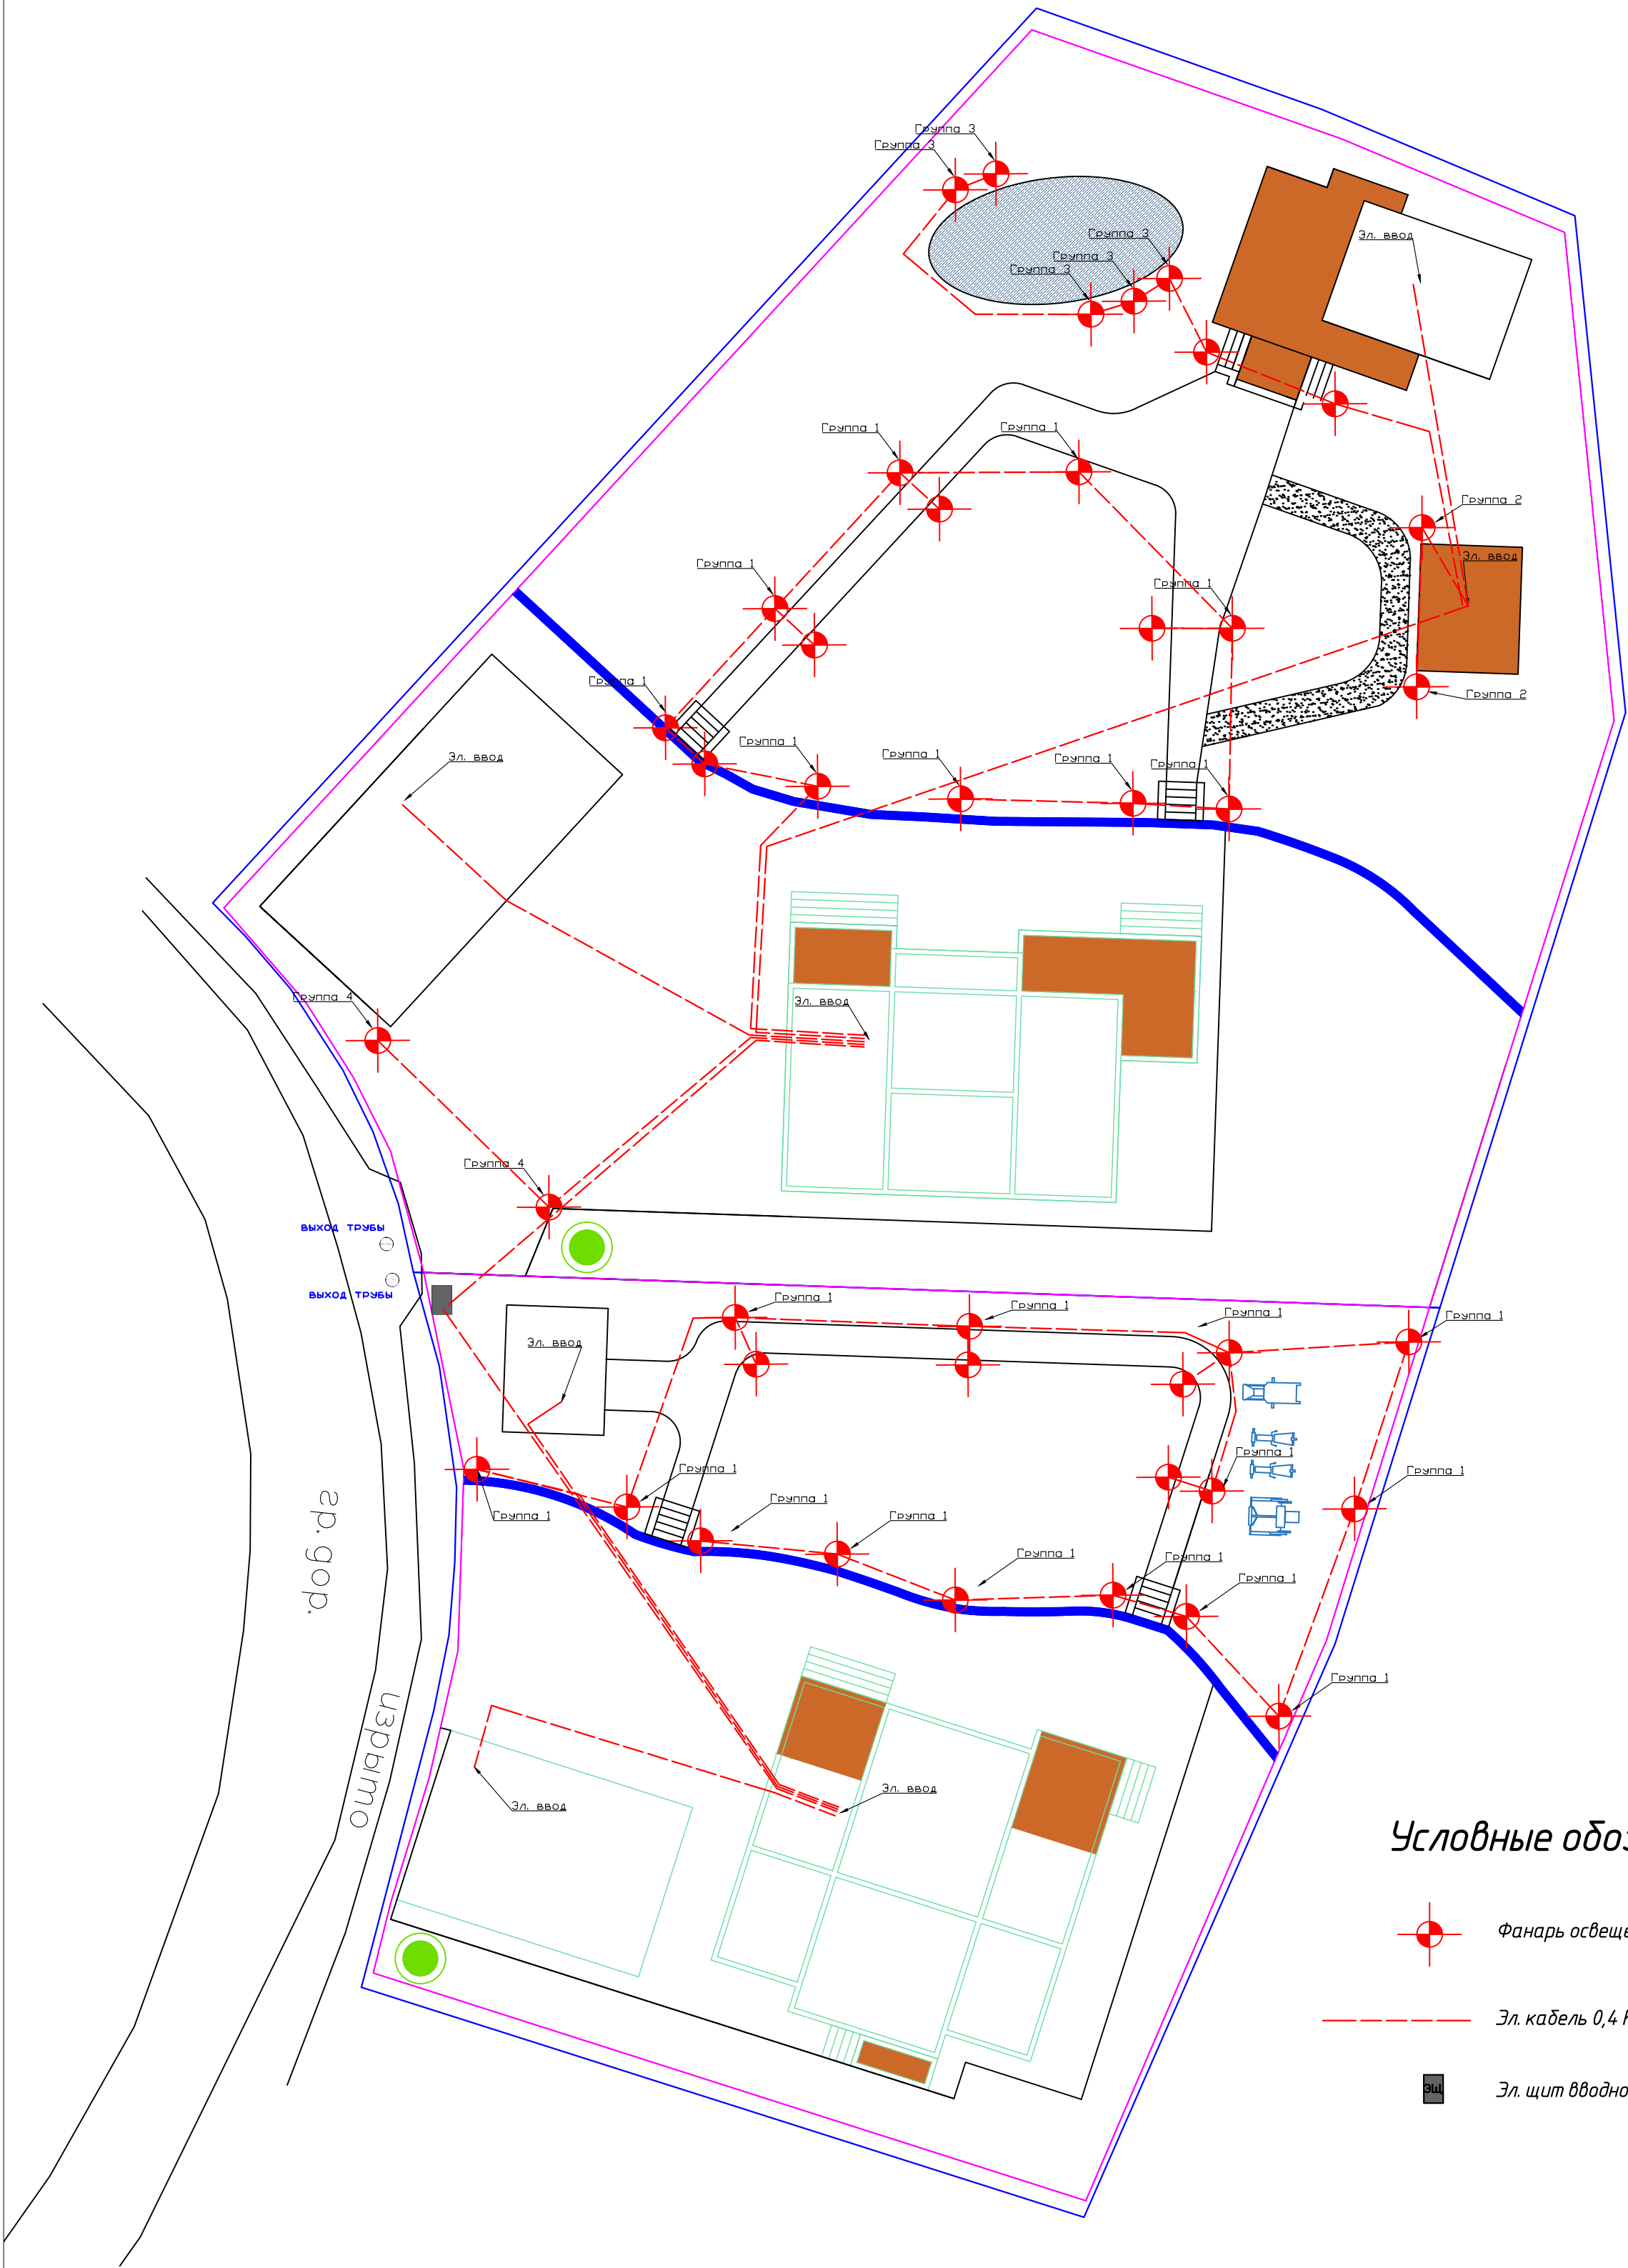

Условные обозначения:

-  Фанарь освещения
-  Эл. кабель 0,4 Кв
-  Эл. щит вводной


					ДСП № 12/08-РП			
					Адрес: Ленинградская область, Приозерский муниципальный округ			
Должность	Ф.И.О.	Подпись	Дата		Индивидуальный жилой дом	Стадия	Лист	Листов
Ген. дир.	Анцеловский					П		
Гл. инж.	Базров							
Геодезист	Мисак							
					Наружное освещение		ООО "Аракс"	

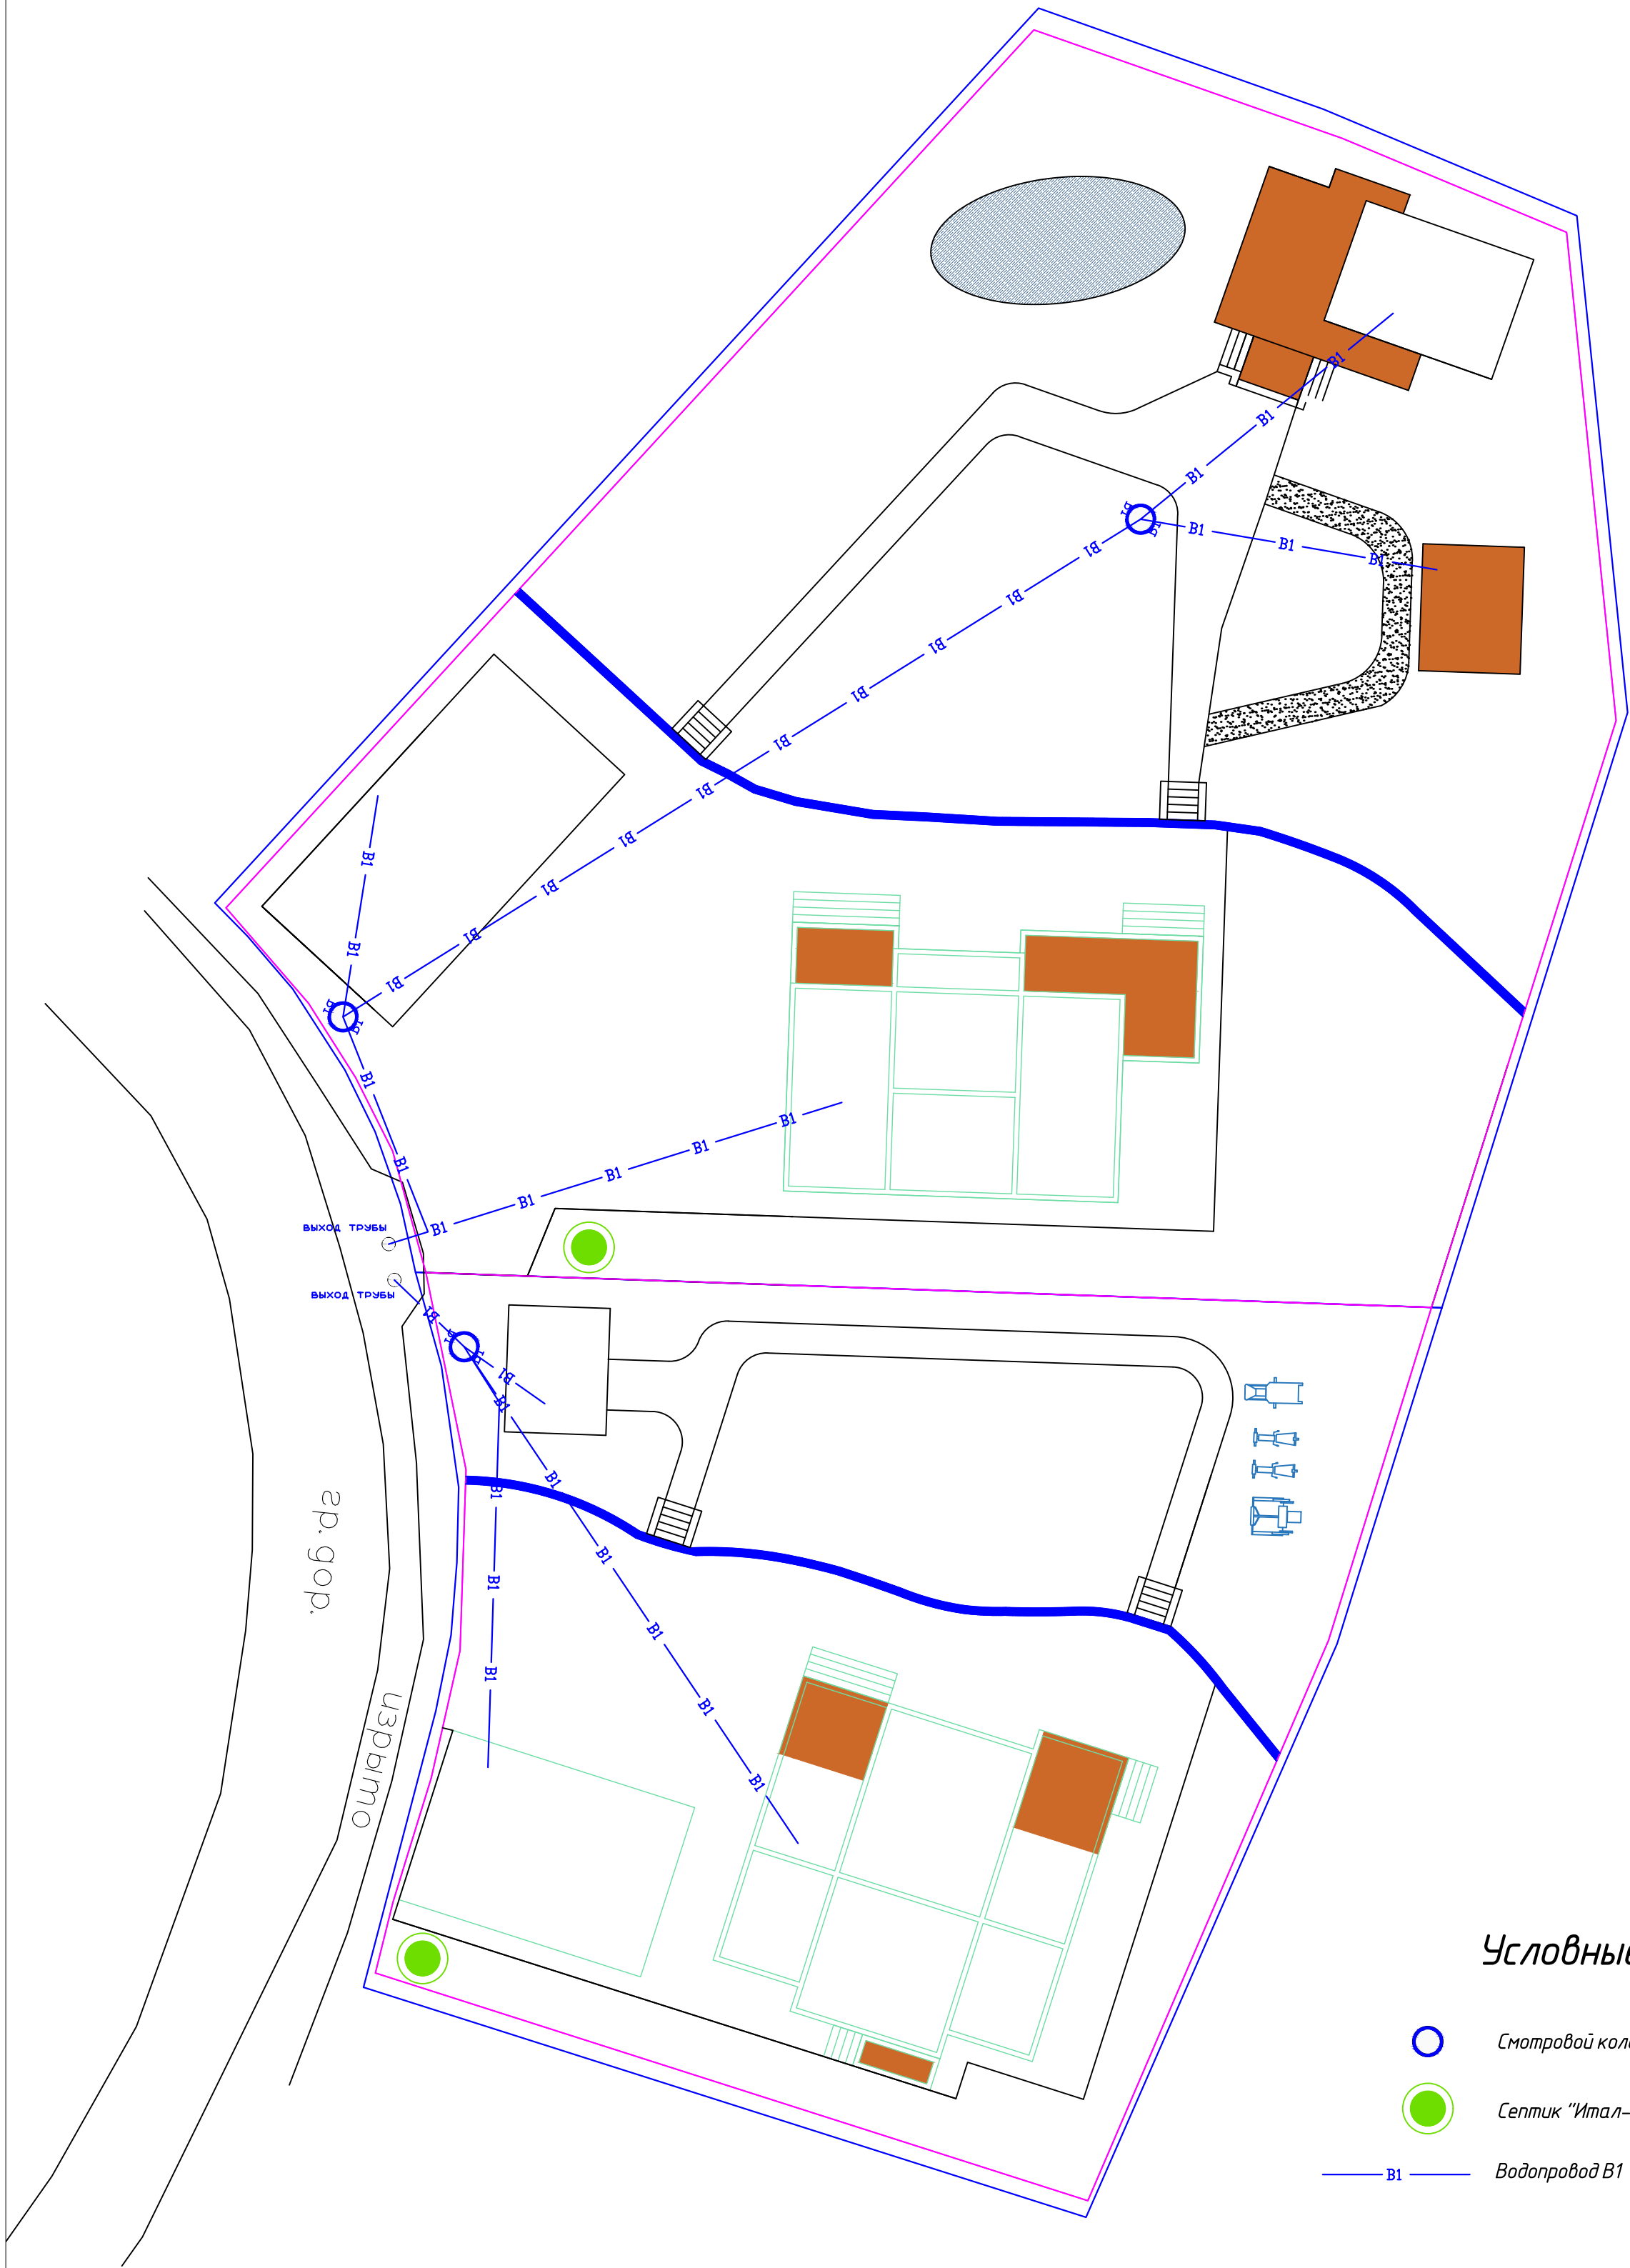

Условные обозначения:

- Смотровой колодец водопроводный В1
- Септик "Итал-Био"
- В1 — Водопровод В1

				ДСП № 12/08-РП			
				Адрес: Ленинградская область, Приозерский муниципальный округ			
Должность	Ф. И. О.	Подпись	Дата	Индивидуальный жилой дом	Стадия	Лист	Листов
Ген. дир.	Анцеловский				П		
Гл. инж.	Базров						
Геодезист	Мисак						
				Водопровод		ООО "Аракс"	

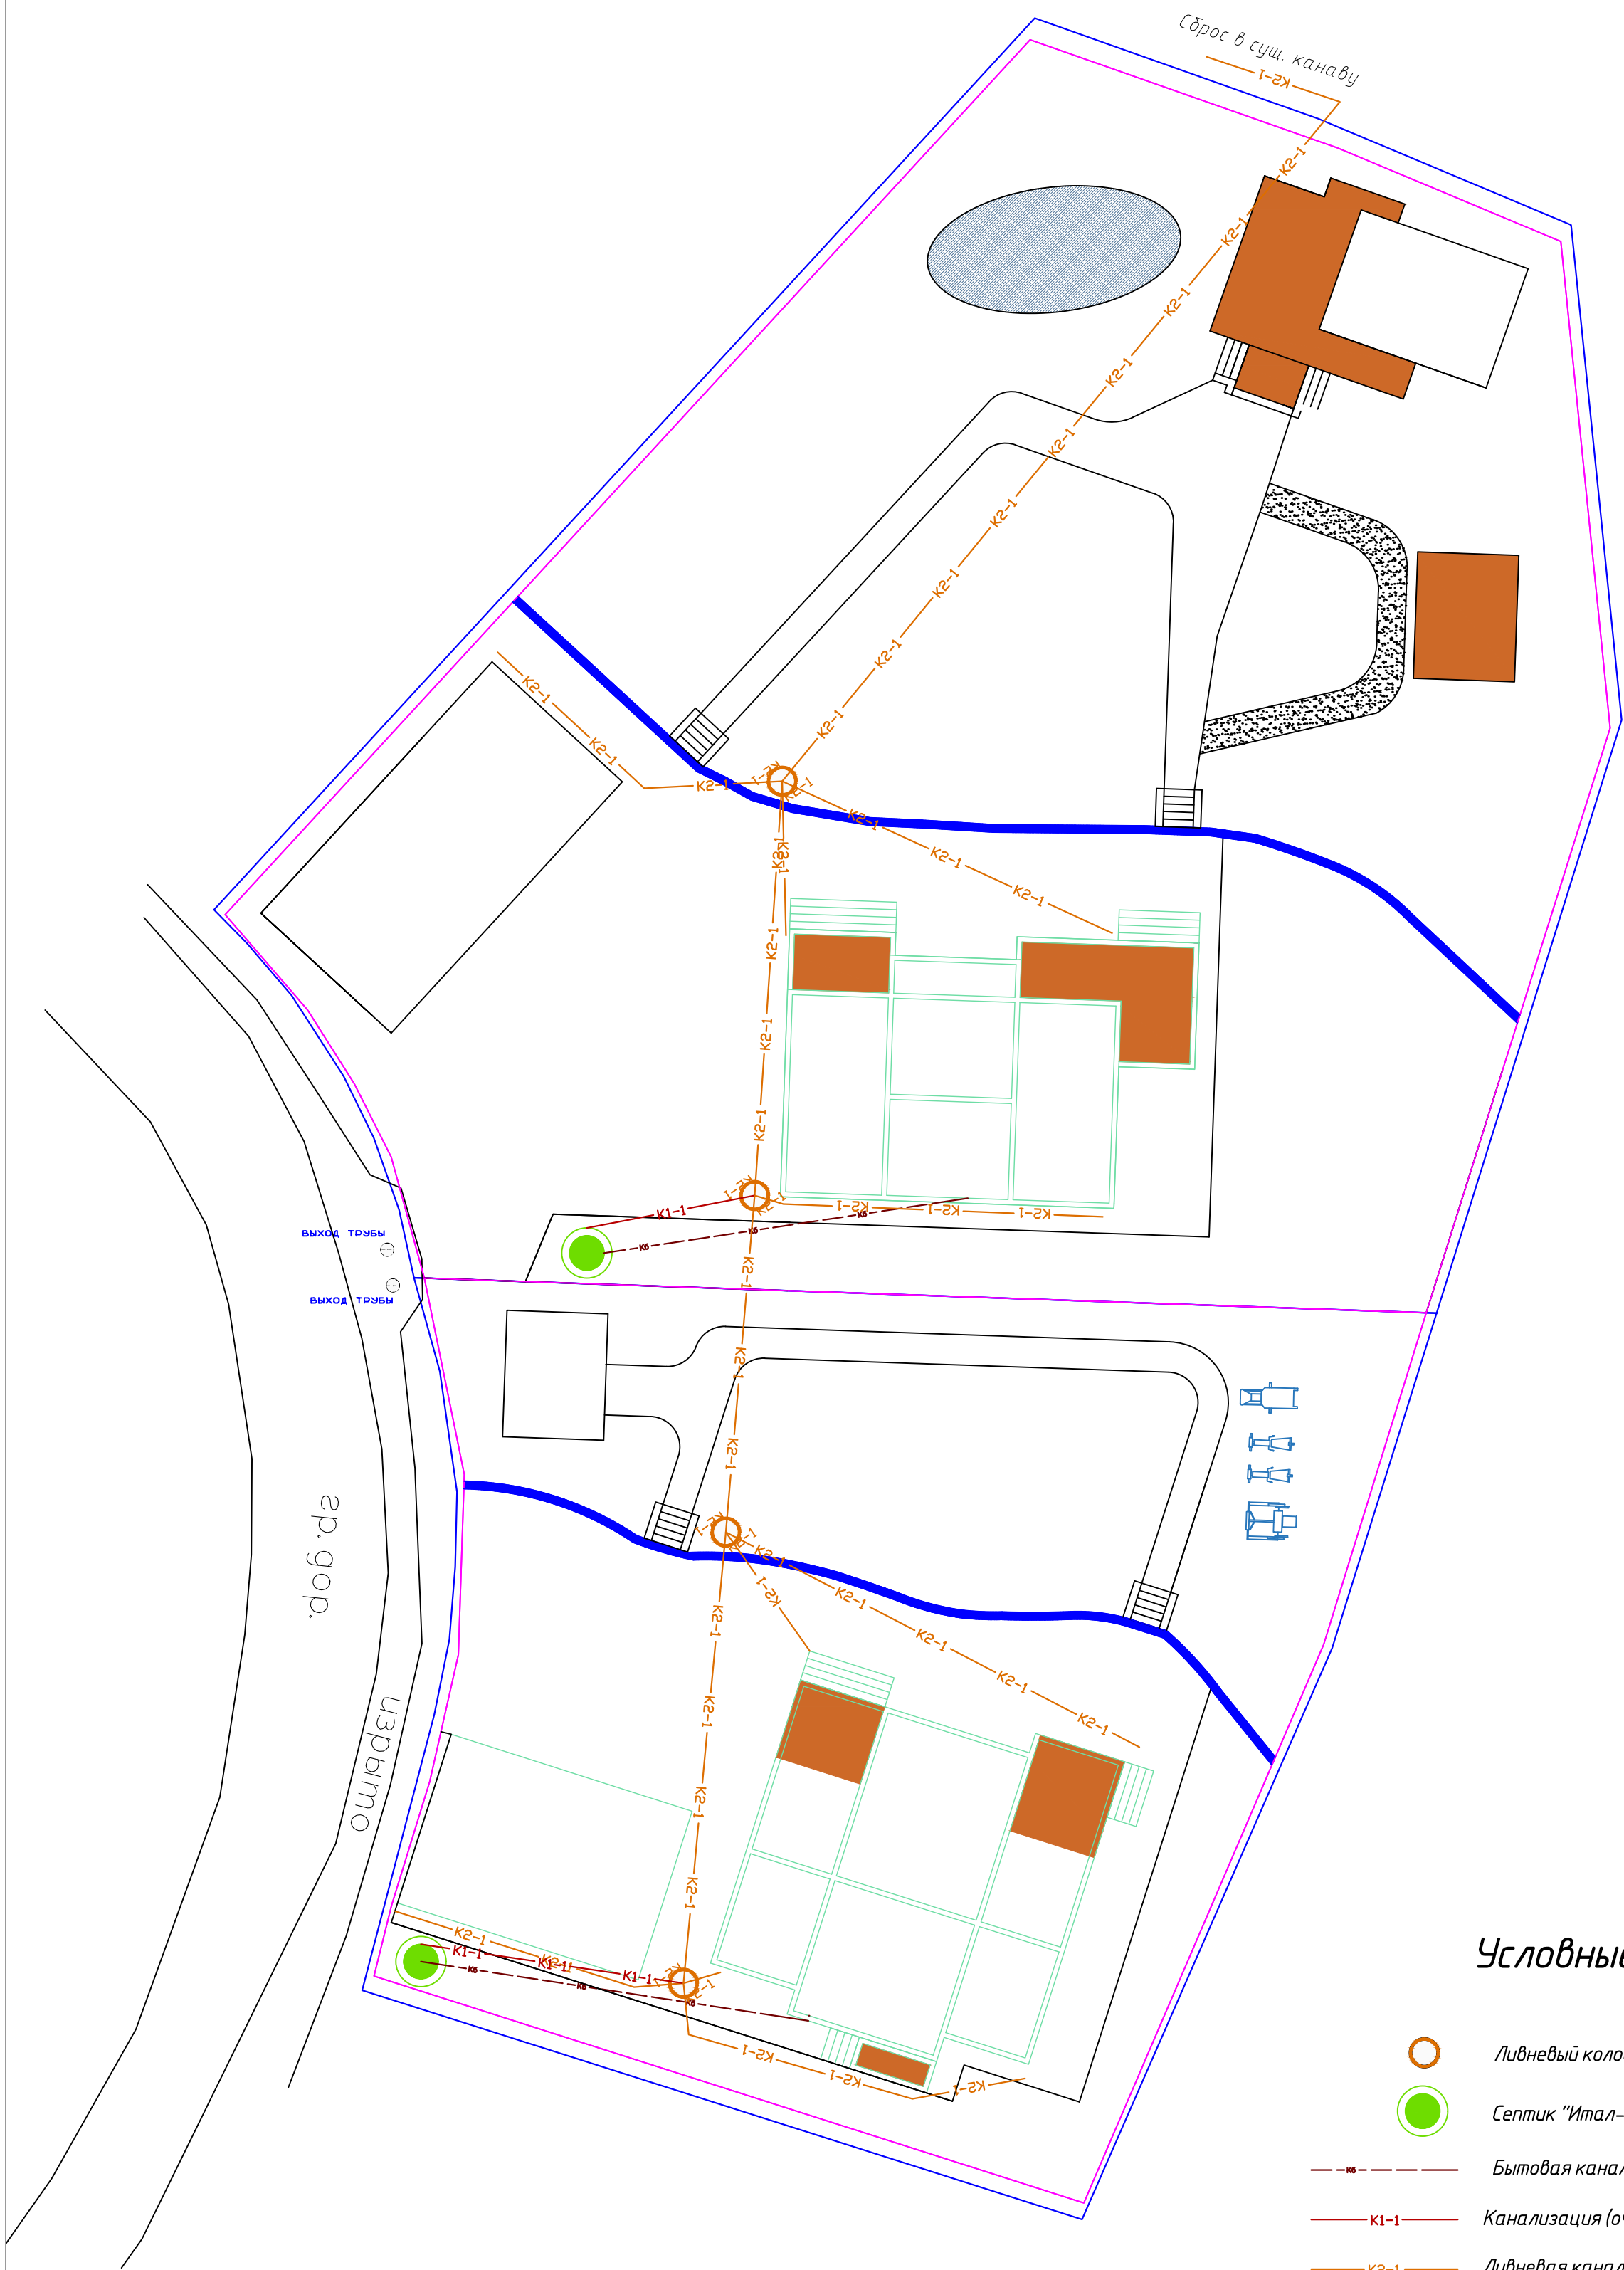

Условные обозначения:

- Ливневый колодец K2-1
- Септик "Итал-Био"
- Бытовая канализация K0
- Канализация (очищенная) K1-1
- Ливневая канализация K2-1

				ДСП № 12/08-РП			
				Адрес: Ленинградская область, Приозерский муниципальный округ			
Должность	Ф. И. О.	Подпись	Дата	Индивидуальный жилой дом	Стадия	Лист	Листов
Ген. дир.	Анцеловский				П		
Гл. инж.	Базров						
Геодезист	Мисак						
				Канализация	ООО "Аракс"		